TEKLED

TURAN 12 KATLI KONUT BLOKLARI

ELEKTRİK PANOLARI ÜRETİM ONAY DOSYASI


MÜŞTERİ ONAY NÜSHASI

BPУ-1	**BPУ1-11-10**
BPУ-2	**BPУ1-48-03**
BPУ-3 c ABP	**BPУ1-17-70**
REVİZYON / TARİH	**R1 / 07.08.2026**

TASARIM	KONTROL	ÜRETİM	KALİTE	PROJE	PANO	İŞ EMRİ	SAYFA
TEKLED				TURAN			1

ВРУ-1 - GENEL ONAY ВРУ1-11-10

PANO ADI	ВРУ-1	PROJE KODU	ВРУ1-11-10
ÖLÇÜ	1700 x 800 x 450 mm + 100 mm kaide	TİP	Dikili tip metal pano

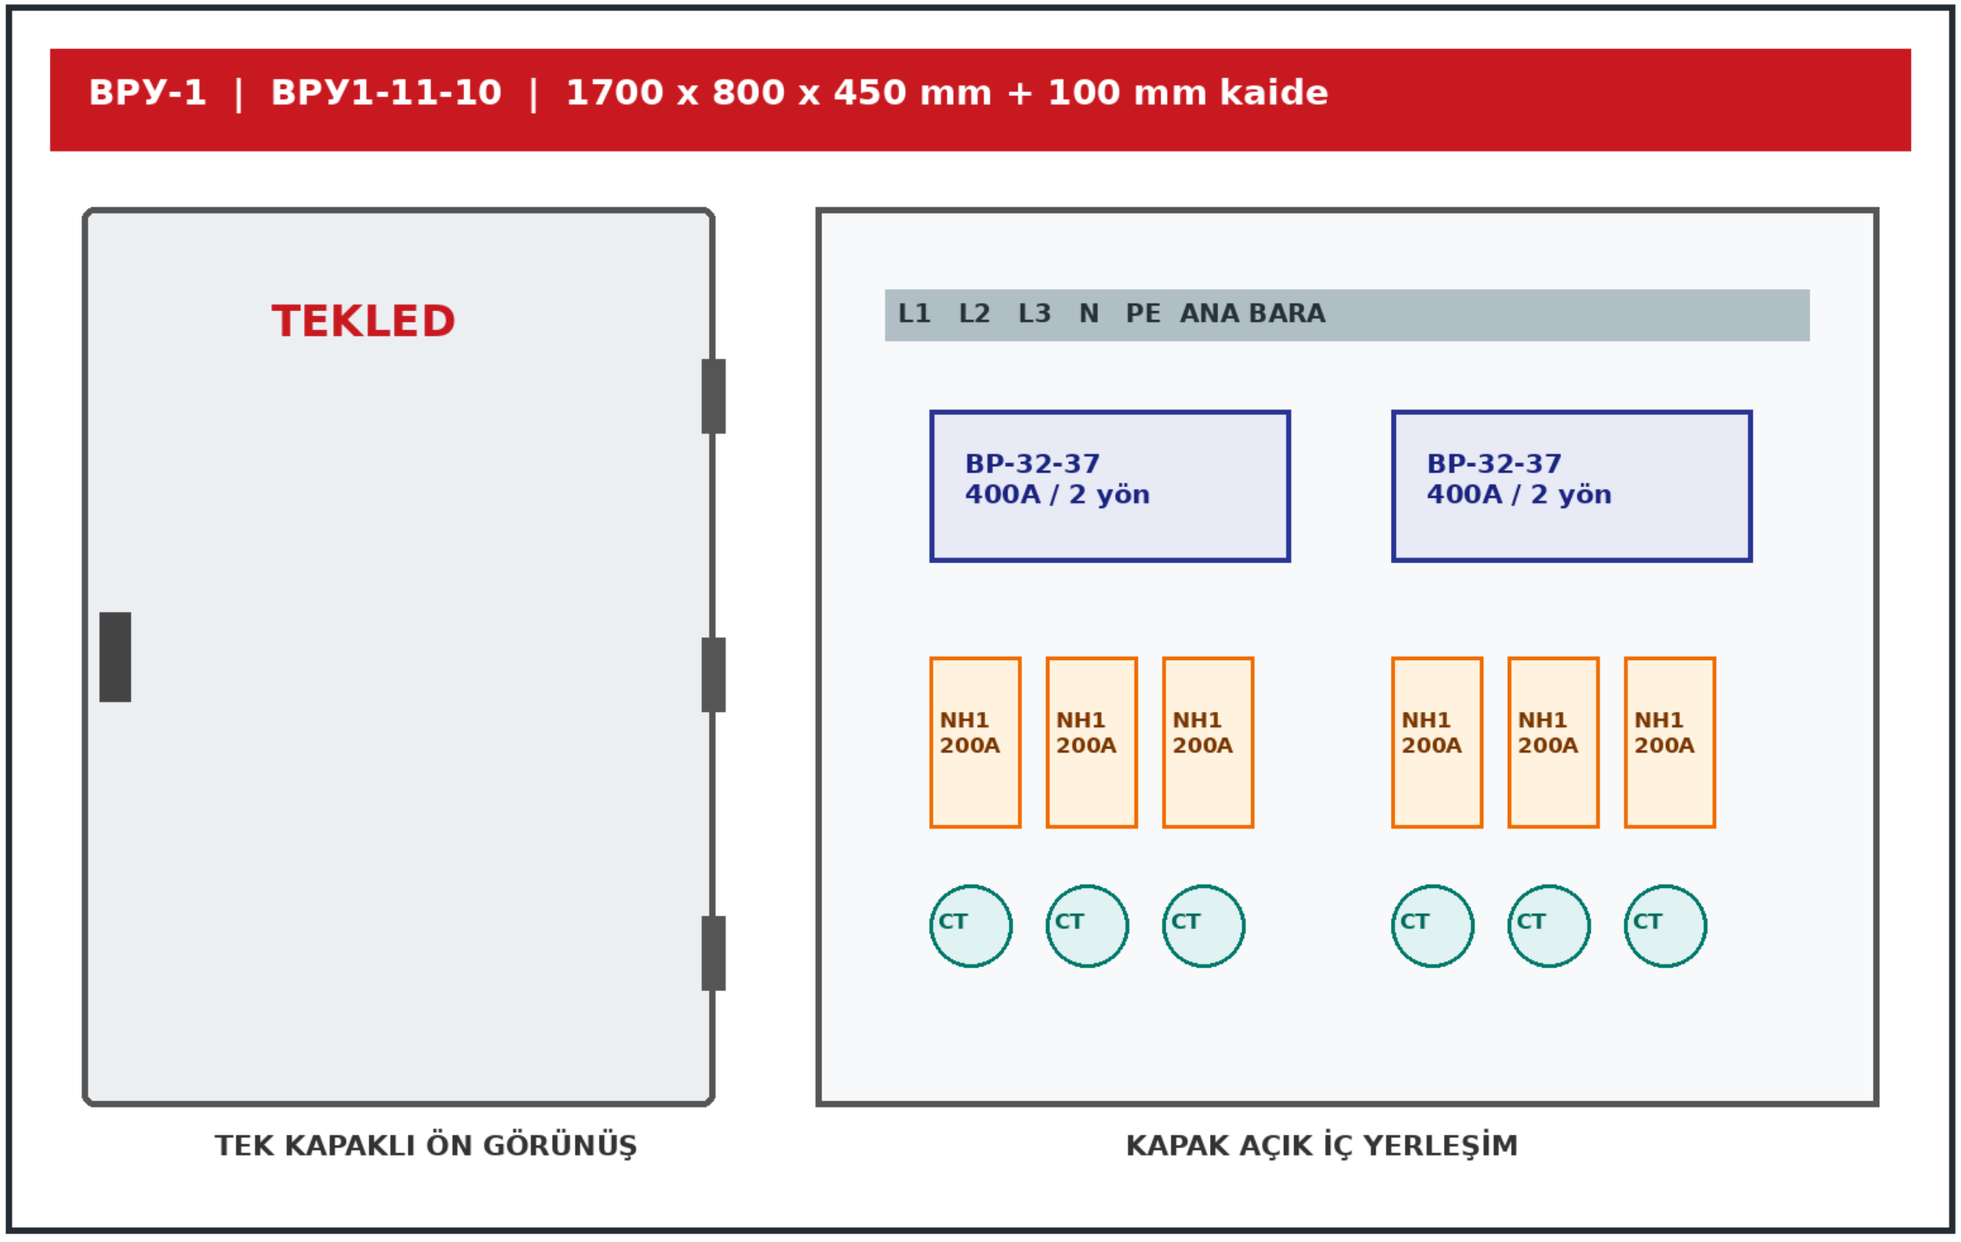


Korpus tek kapaklıdır; dışarıdan bakıldığında kapı kolu solda, menteşeler sağdadır. Tüm ana ve dağıtım baraları alüminyumdur. Onay kapsamı: dış görünüş, ölçü, pano tipi ve cihaz yerleşim prensibi.

TASARIM	KONTROL	ÜRETİM	KALİTE	PROJE	PANO	İŞ EMRİ	SAYFA
TEKLED				TURAN			2

ВРУ-1 - TEK HAT REFERANSI

Kaynak proje pafta 3

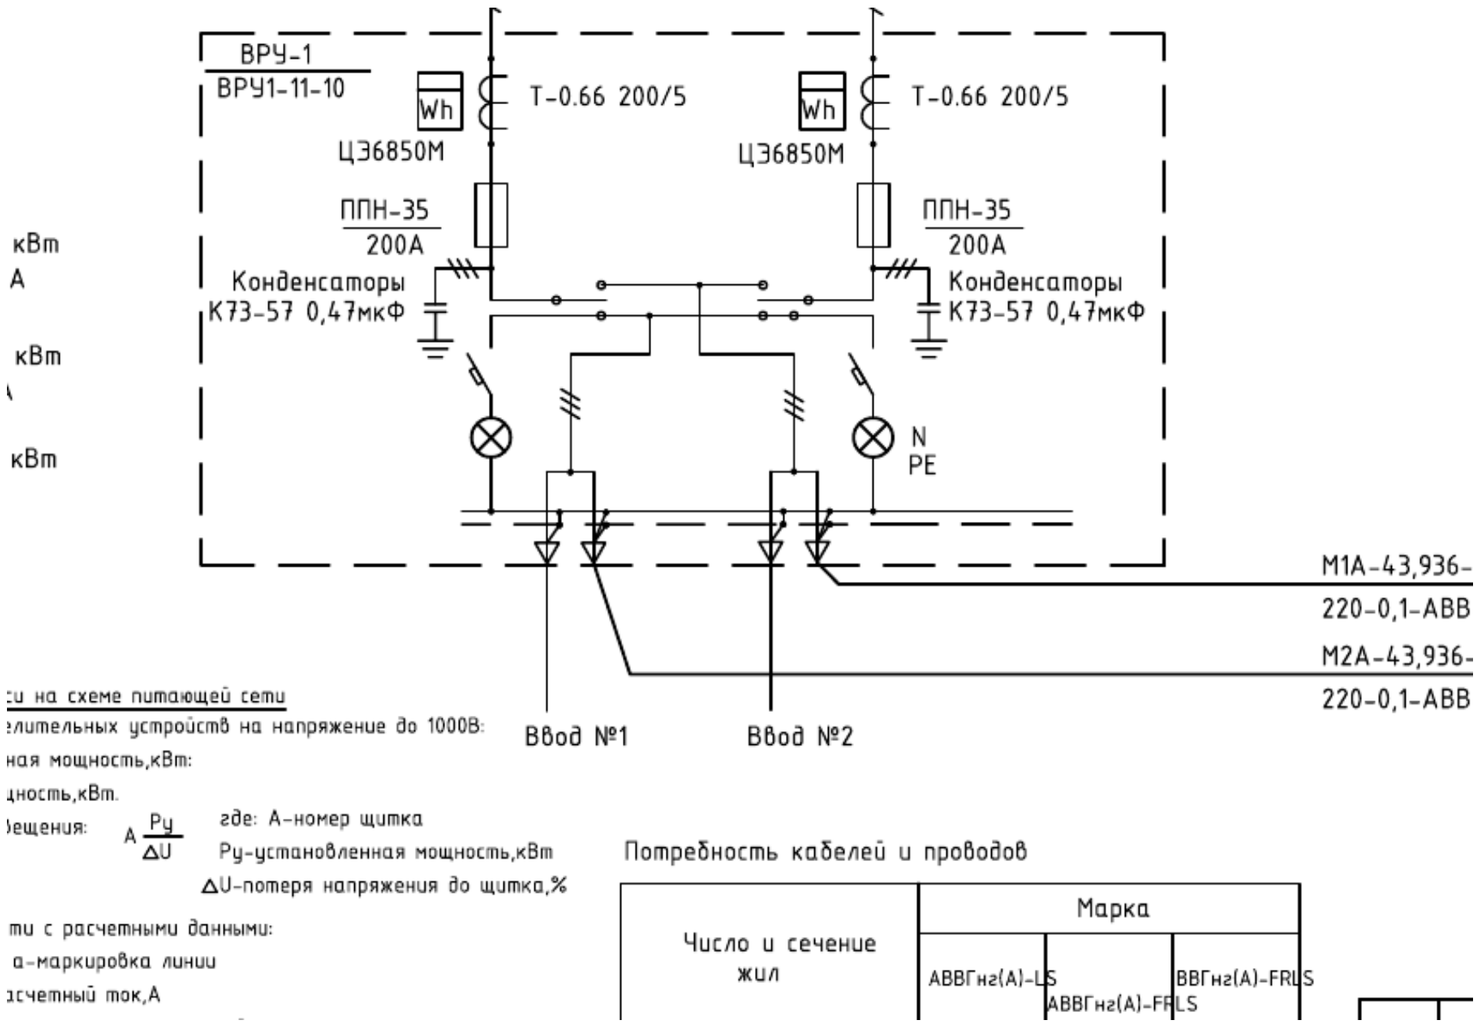


Bu sayfadaki tek hat yalnız ilgili reçete panosuna aittir.

TASARIM	KONTROL	ÜRETİM	KALİTE	PROJE	PANO	İŞ EMRİ	SAYFA
TEKLED				TURAN			3

BPУ-2 - GENEL ONAY BPУ1-48-03

PANO ADI	BPУ-2	PROJE KODU	BPУ1-48-03
ÖLÇÜ	1700 x 800 x 450 mm + 100 mm kaide	TİP	Dikili tip metal dağıtım panosu

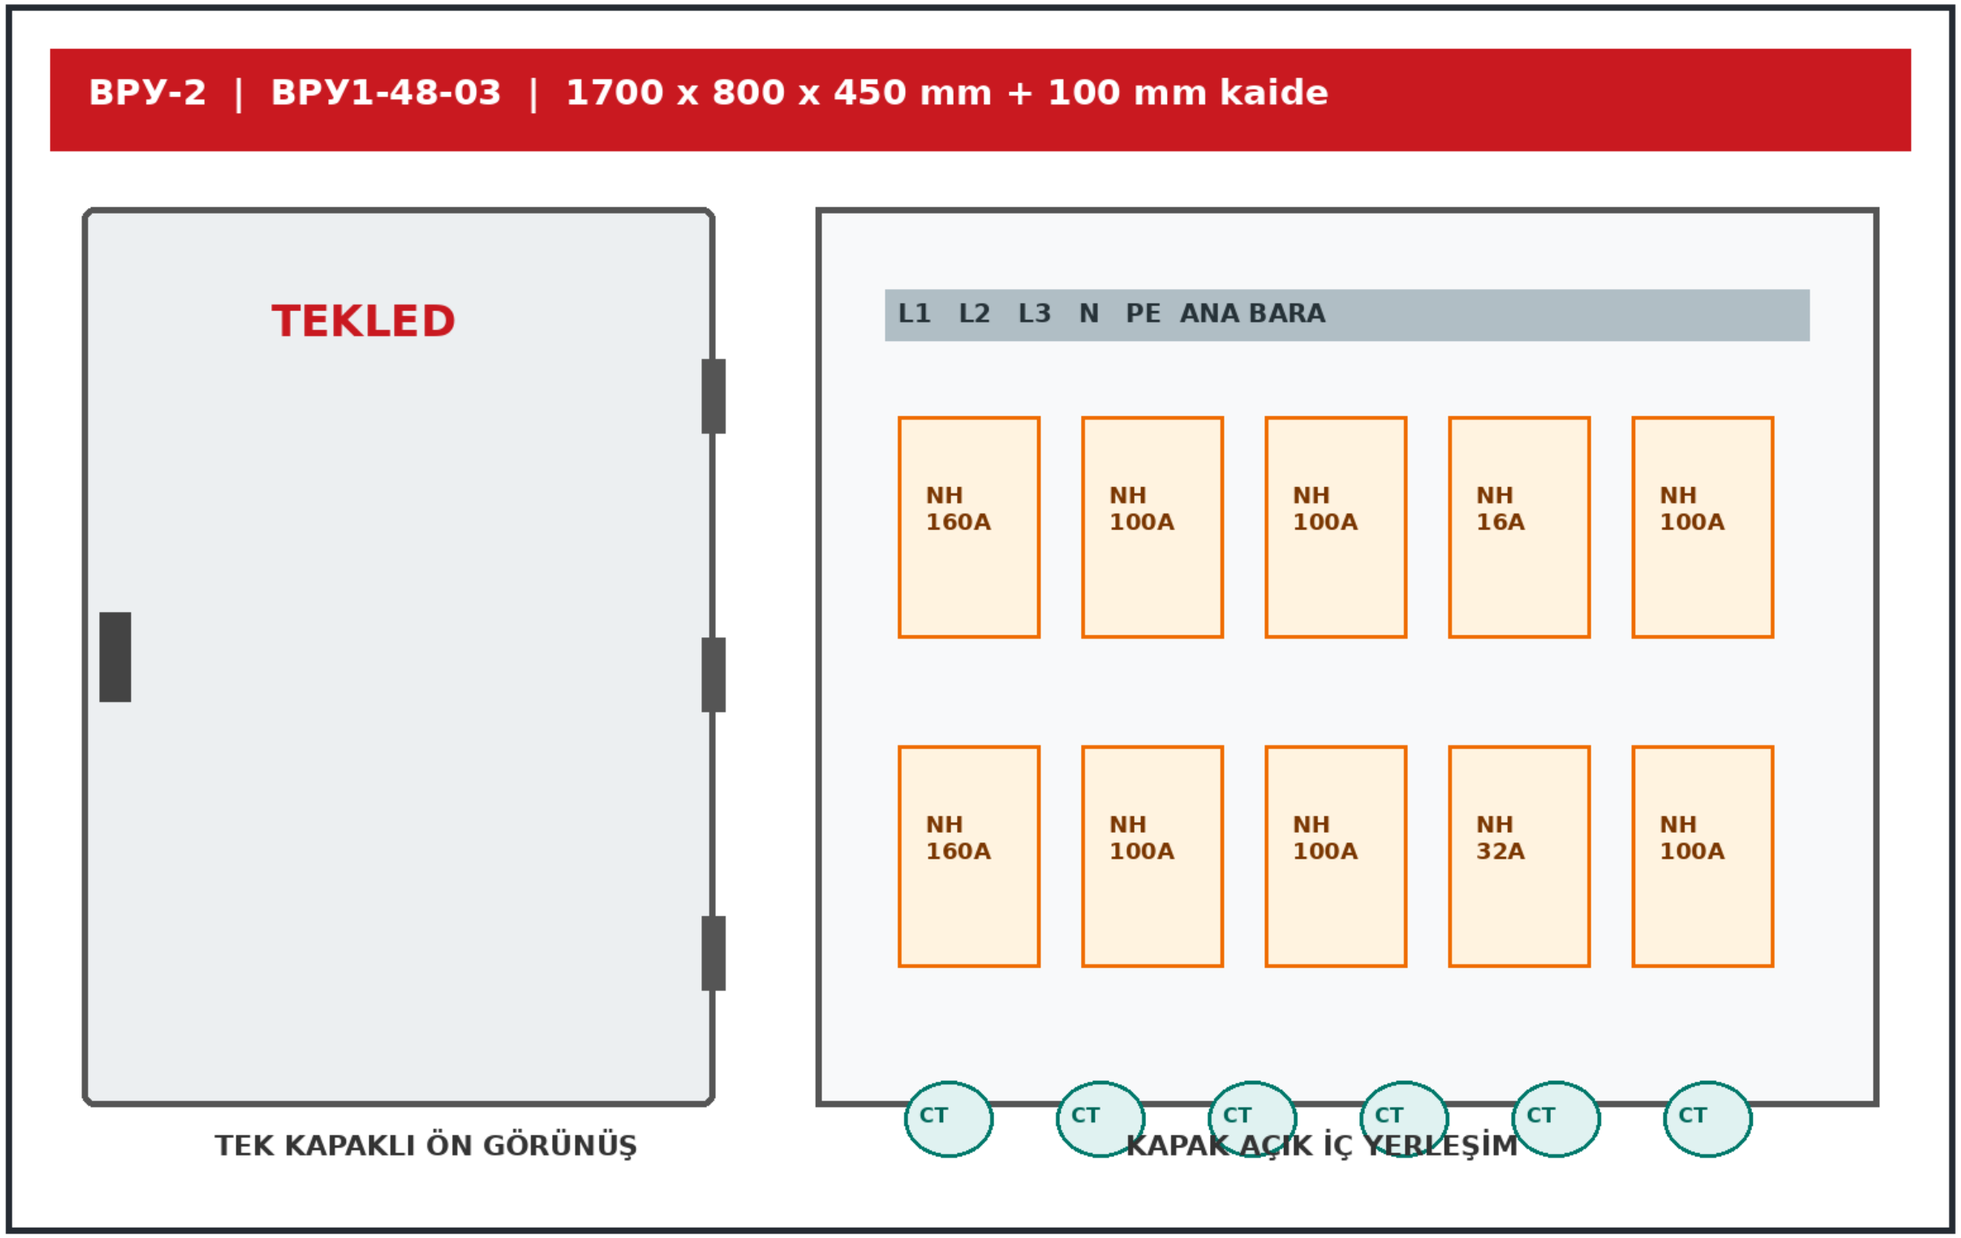


Korpus tek kapaklıdır; dışarıdan bakıldığında kapı kolu solda, menteşeler sağdadır. Tüm ana ve dağıtım baraları alüminyumdur. Onay kapsamı: dış görünüş, ölçü, pano tipi ve cihaz yerleşim prensibi.

TASARIM	KONTROL	ÜRETİM	KALİTE	PROJE	PANO	İŞ EMRİ	SAYFA
TEKLED				TURAN			4

ВРУ-2 - TEK HAT REFERANSI

Kaynak proje pafta 3

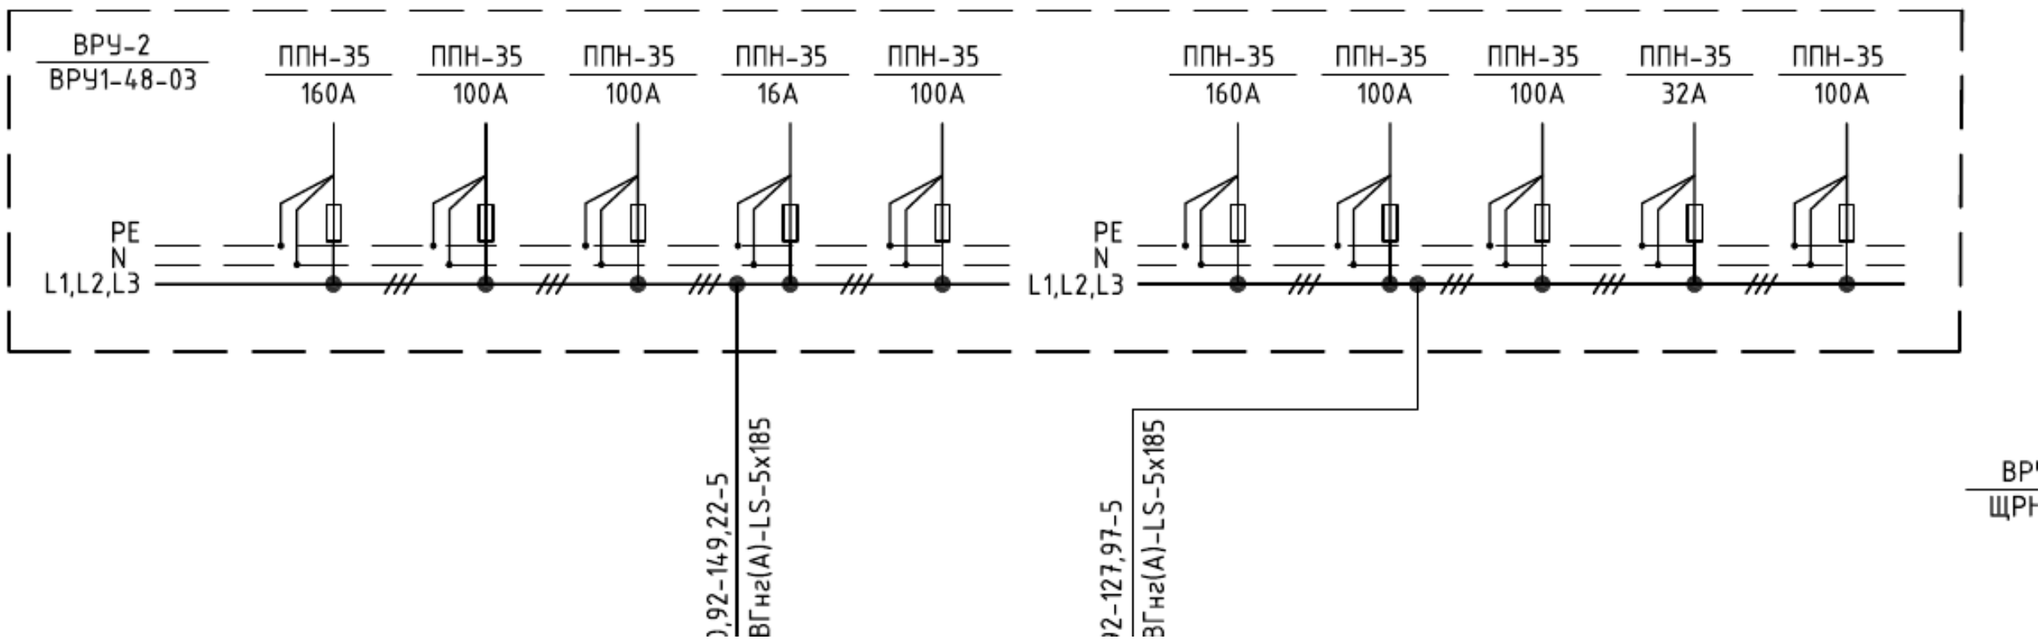


Bu sayfadaki tek hat yalnız ilgili reçete panosuna aittir.

TASARIM	KONTROL	ÜRETİM	KALİTE	PROJE	PANO	İŞ EMRİ	SAYFA
TEKLED				TURAN			5

ВРУ-3 с АВР - GENEL ONAY ВРУ1-17-70

PANO ADI	ВРУ-3 с АВР	PROJE KODU	ВРУ1-17-70
ÖLÇÜ	1600 x 600 x 400 mm + 100 mm kaide	TİP	Dikili tip metal ATS panosu

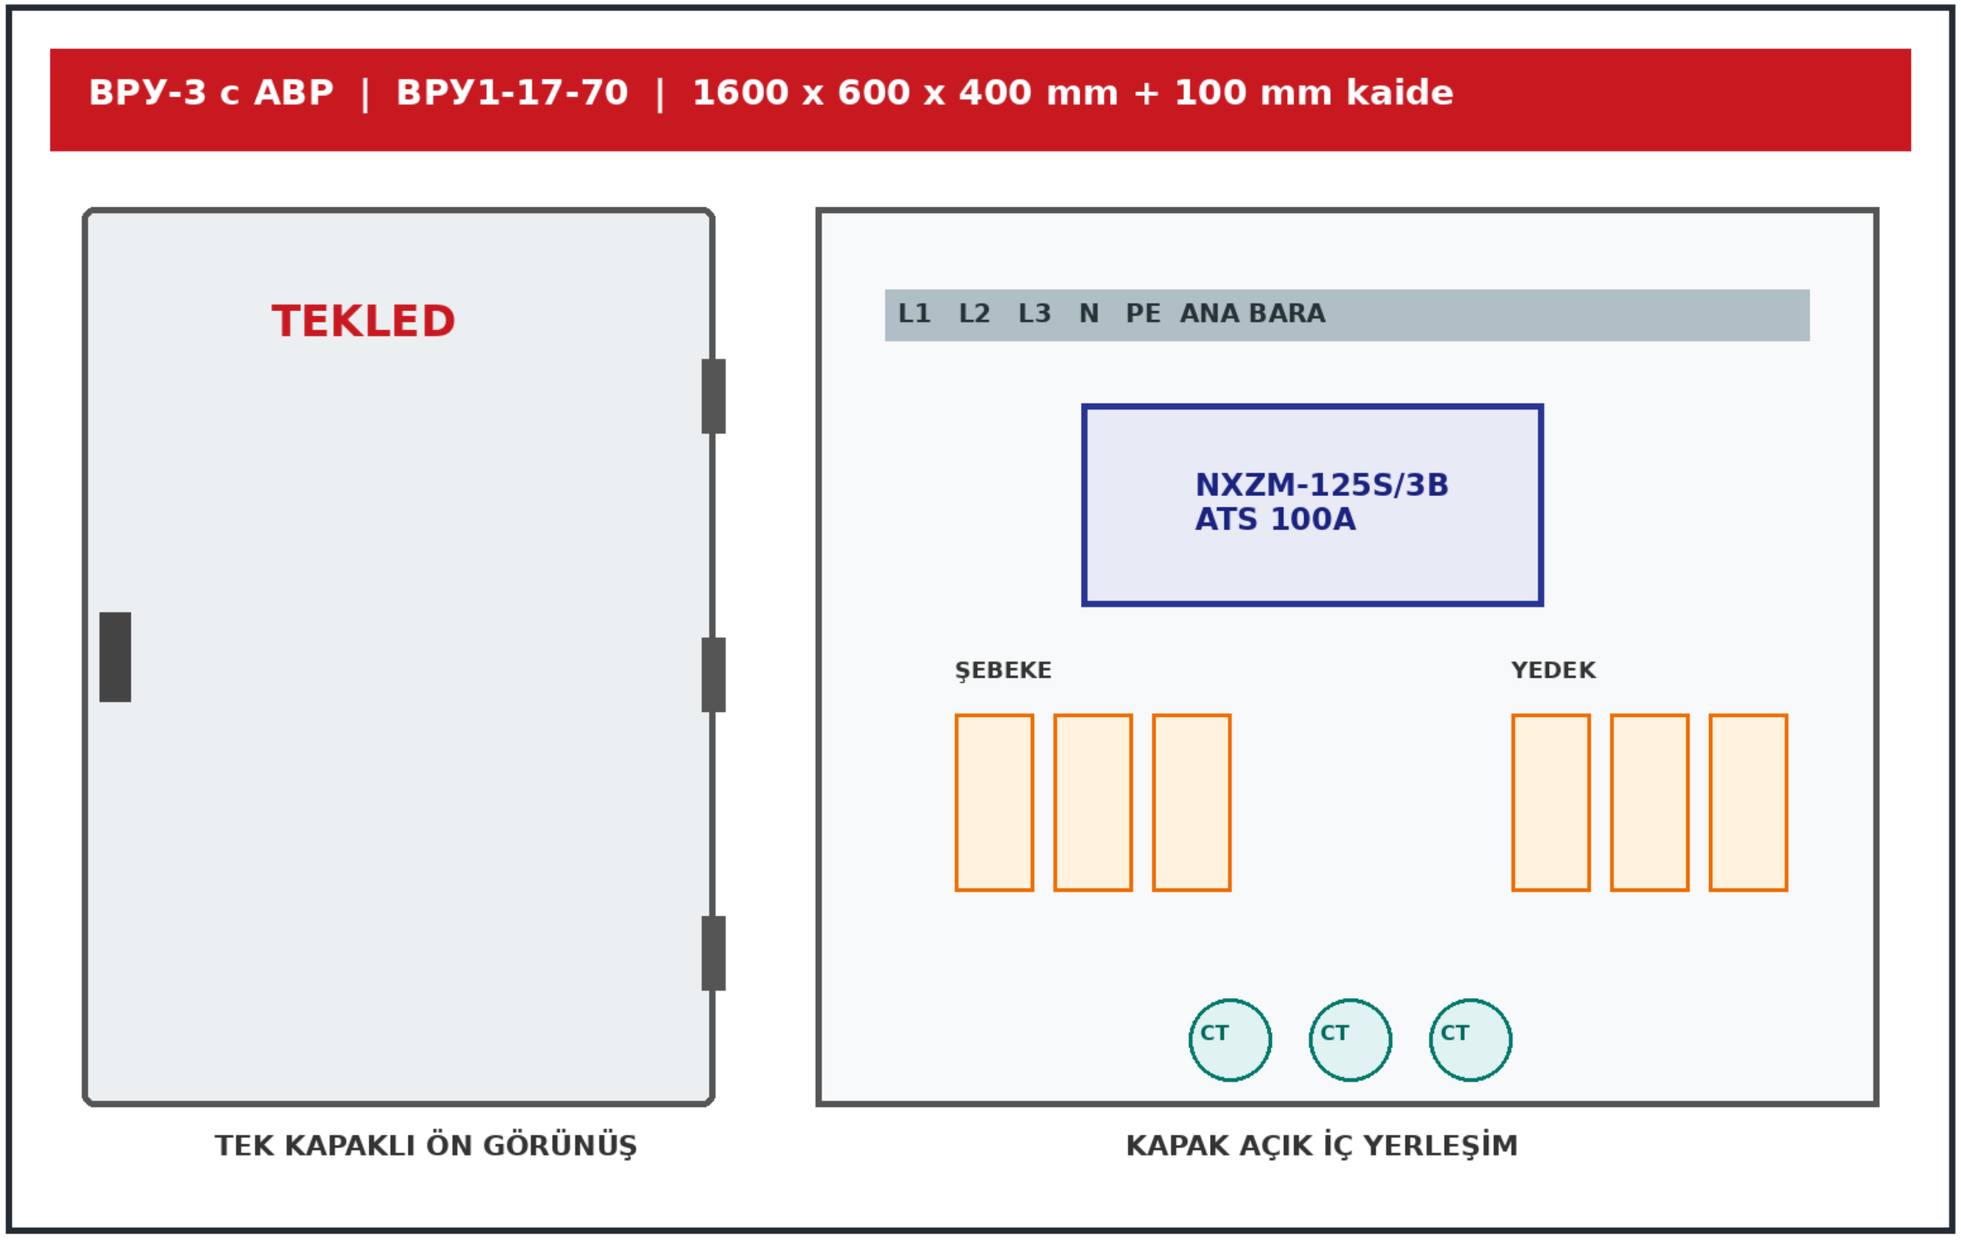


Korpus tek kapaklıdır; dışarıdan bakıldığında kapı kolu solda, menteşeler sağdadır. Tüm ana ve dağıtım baraları alüminyumdur. Onay kapsamı: dış görünüş, ölçü, pano tipi ve cihaz yerleşim prensibi.

TASARIM	KONTROL	ÜRETİM	KALİTE	PROJE	PANO	İŞ EMRİ	SAYFA
TEKLED				TURAN			6

ВРУ-3 с АВР - TEK HAT REFERANSI

Kaynak proje pafta 3

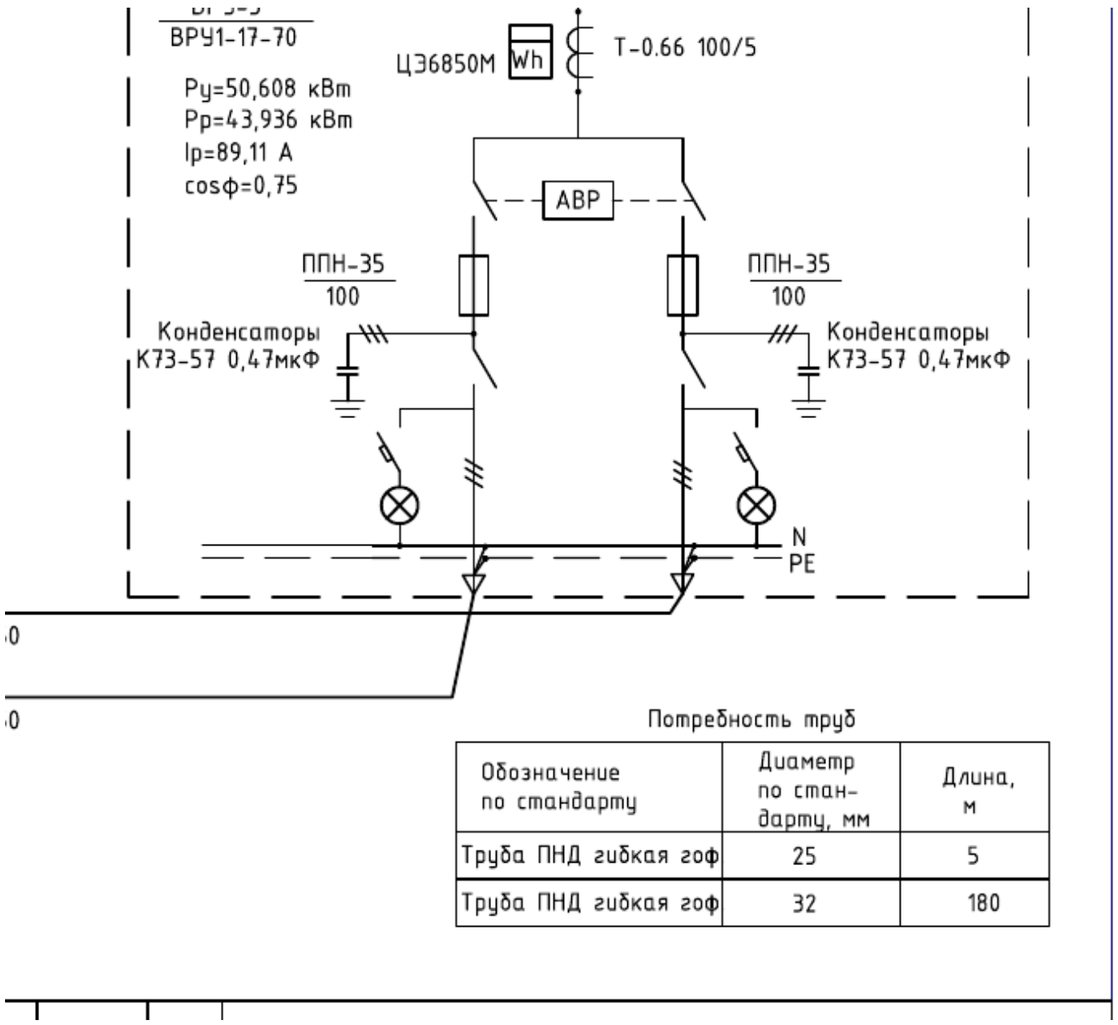

Потребность труб

Обозначение по стандарту	Диаметр по стан-дарту, мм	Длина, м
Труба ПНД гибкая гоф	25	5
Труба ПНД гибкая гоф	32	180

Bu sayfadaki tek hat yalnız ilgili reçete panosuna aittir.

TASARIM	KONTROL	ÜRETİM	KALİTE	PROJE	PANO	İŞ EMRİ	SAYFA
TEKLED				TURAN			7